This drawing is the property of HABITAT DESIGN CONSULTANTS
must not be passed on to any person or body not authorised by us to receive it nor be copied orotherwise made use either in full or in part by such person or body without our prior permission in writing

Project Title:-
Residence for Mr.
CHAWLA
Sector 15-B Chandigarh

NOTE

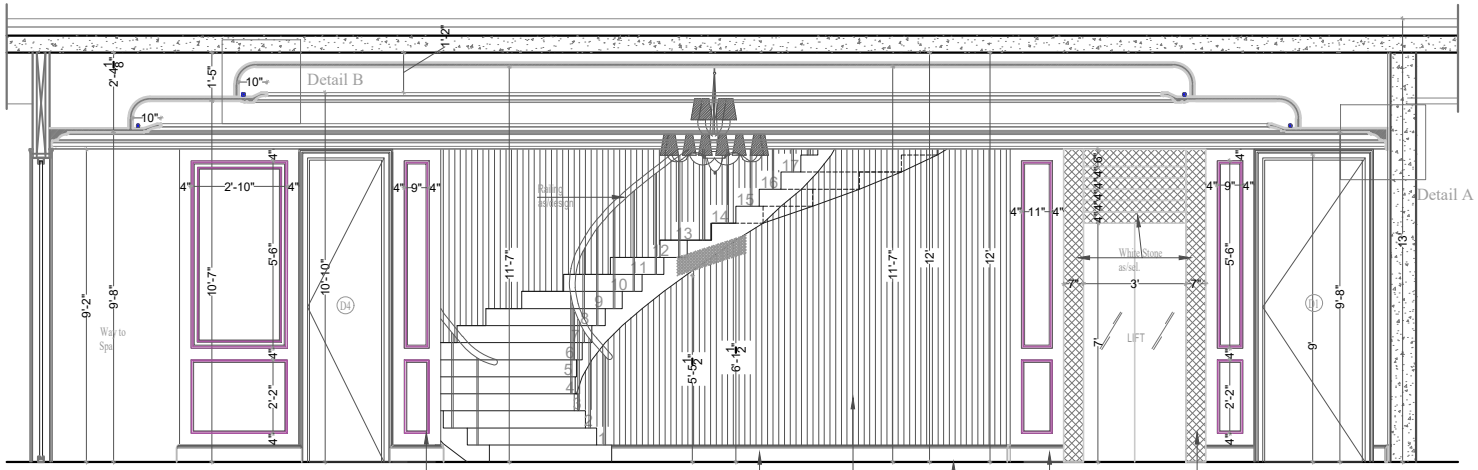

Basement Section at B-B'

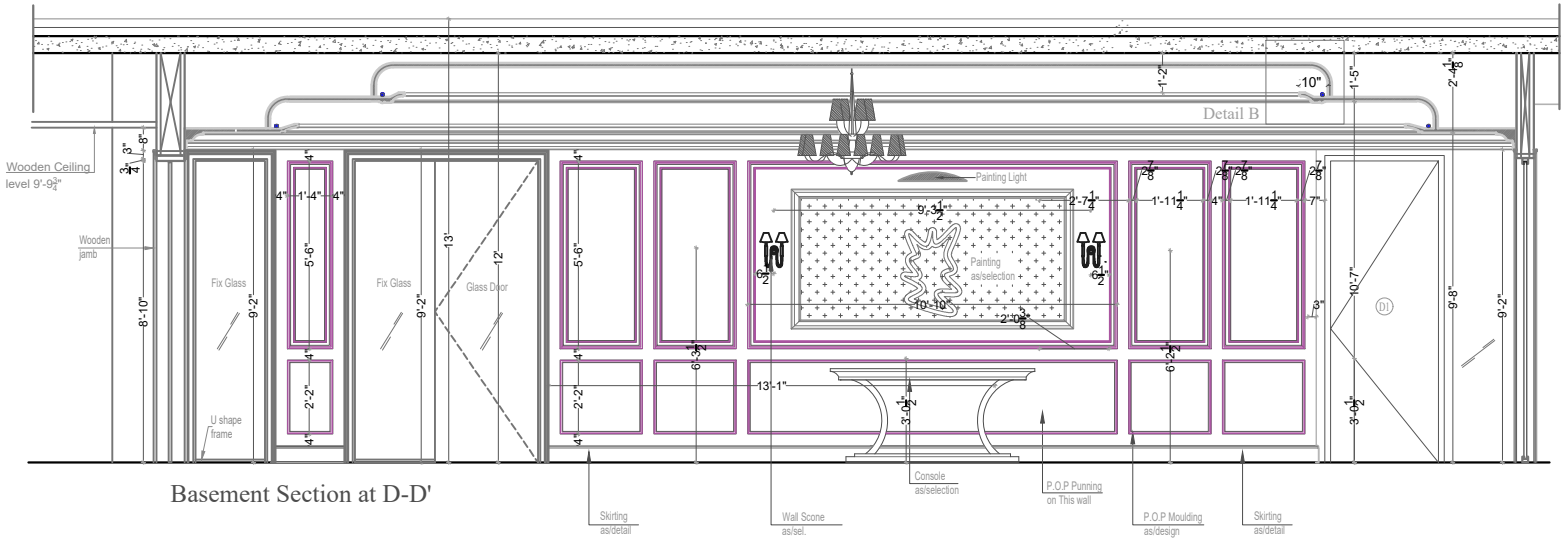

Basement Section at D-D'

S.No.	DATE	REVISION

RELEASED FOR: ☐ PRELIMINARY ☐ TENDER ☐ APPROVAL ☑ IDCS FOR CONSTRUCTION

NOTES:-

DRAWING TITLE:
Basement Lobby Wall Elevations

SCALE: N.T.S

DATE: 09.04.25

DEALT BY: ROHIT

DWG Name: INT_LB_LT-01

ARCHITECT:
Habitat design consultants
1777, Maharaj nagar
Ludhiana
Tel/fax - 0161-4689202